

Spatial Taxonomy — Key Plans and Tiles — Professional Centres and Suburban Office

Woodfine Management Corp.

Jennifer M. Woodfine

January 6, 2026

V3


"Key Plans and Tiles" means a geometric self-similar aperiodic space planning system based on furniture/equipment arrangements and circulation versus modular area per person progressions.

Key Plan square footage from the samples to date:			Initial Design		Key Plan Private Office		Key Plan Laboratory		Key Plan Academic		Key Plan Business		Key Plan Medical		Key Plan Civic		Tile Corporate Office	
Private Office (m2 / SF)																		
Small			-	-	30	325	-	-	-	-	-	-	-	-	-	-	-	-
Medium			-	-	43	465	-	-	-	-	-	-	-	-	-	-	-	-
Large			-	-	64	685	-	-	-	-	-	-	-	-	-	-	-	-
Total			-	-	137	1,475	-	-	-	-	-	-	-	-	-	-	-	-
Professional Office (m2 / SF)																		
Small			130	1,400	-	-	195	2,099	105	1,131	311	3,350	223	2,402	270	2,912	-	-
Medium			-	-	-	-	316	3,401	240	2,583	400	4,302	331	3,568	577	6,215	-	-
Large			-	-	-	-	401	4,313	378	4,070	669	7,524	486	5,231	822	8,850	-	-
Total			130	1,400	-	-	912	9,813	723	7,784	1,380	15,176	1,040	11,201	1,669	17,977	-	-
Combinations *																		
Small + Small			260	2,800	60	650	390	4,198	210	2,262	622	6,700	446	2,402	540	5,824	-	-
Small + Medium			-	-	73	790	511	5,500	345	3,714	711	7,652	554	5,969	847	9,127	-	-
Small + Large			-	-	94	1,010	596	6,412	483	5,201	980	10,874	709	7,633	1,092	11,762	-	-
Medium + Large			-	-	107	1,150	717	7,714	618	6,653	1,069	11,826	817	8,799	1,399	15,065	-	-
Building Width Calculator (m / ft)																		
Zone 1 — Habitat **			6.0	19'8"	6.0	19'8"	6.8	22'3"	4.7	15'5"	6.0	19'8"	7.2	23'10"	6.0	19'8"	-	-
Zone 2 — Magazine			3.8	12'5"	1.4	4'6"	4.8	15'9"	3.0	3'7"	7.3	23'11"	4.9	16"	7.2	23'8"	-	-
Zone 3 — Corridor			2.0	6'6"	-	-	3.0	10'0"	-	-	2.7	-	2.9	9' 5"	3.6	12'	-	-

Notes

*In the case of Professional Offices, combining either Small + Small or Small + Medium provides for the missing office size between a Professional Office Large and Corporate Office 1/8 Floor.

** With desks placed perpendicular to the façade, be careful, as an extra 0.7 metres is required for proper circulation for three desks in series in Zone 1—Habitat. Without accounting for the circulation, 6 metres exactly to the façade results in only two desks perpendicular to the façade in Zone 1—Habitat rather than three desks.

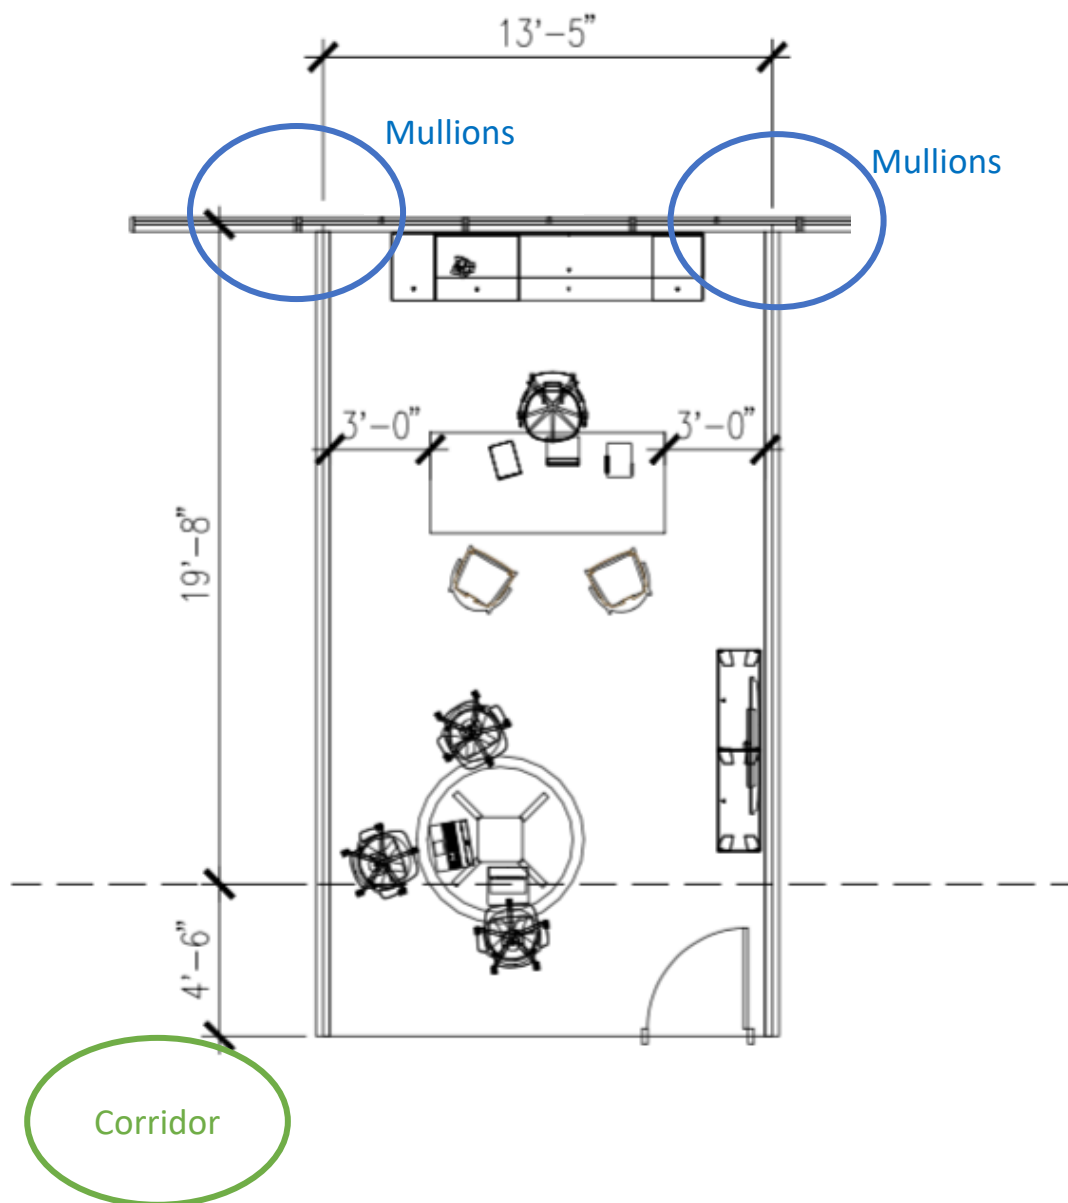

PO 1

325 SF

Private Office
Small

Size: 30m² (325 SF)

Zone 1 — Habitat: 5.9m (19'8")

Zone 2 — Magazine: 1.3m (4'6")


Zone 3 — Corridor: TBD

Reception: 0

Offices: 1

Workstations: 1 / 30 m² (325 SF) per workstation

Occupancy: 6 / 5m² (54 SF) per person

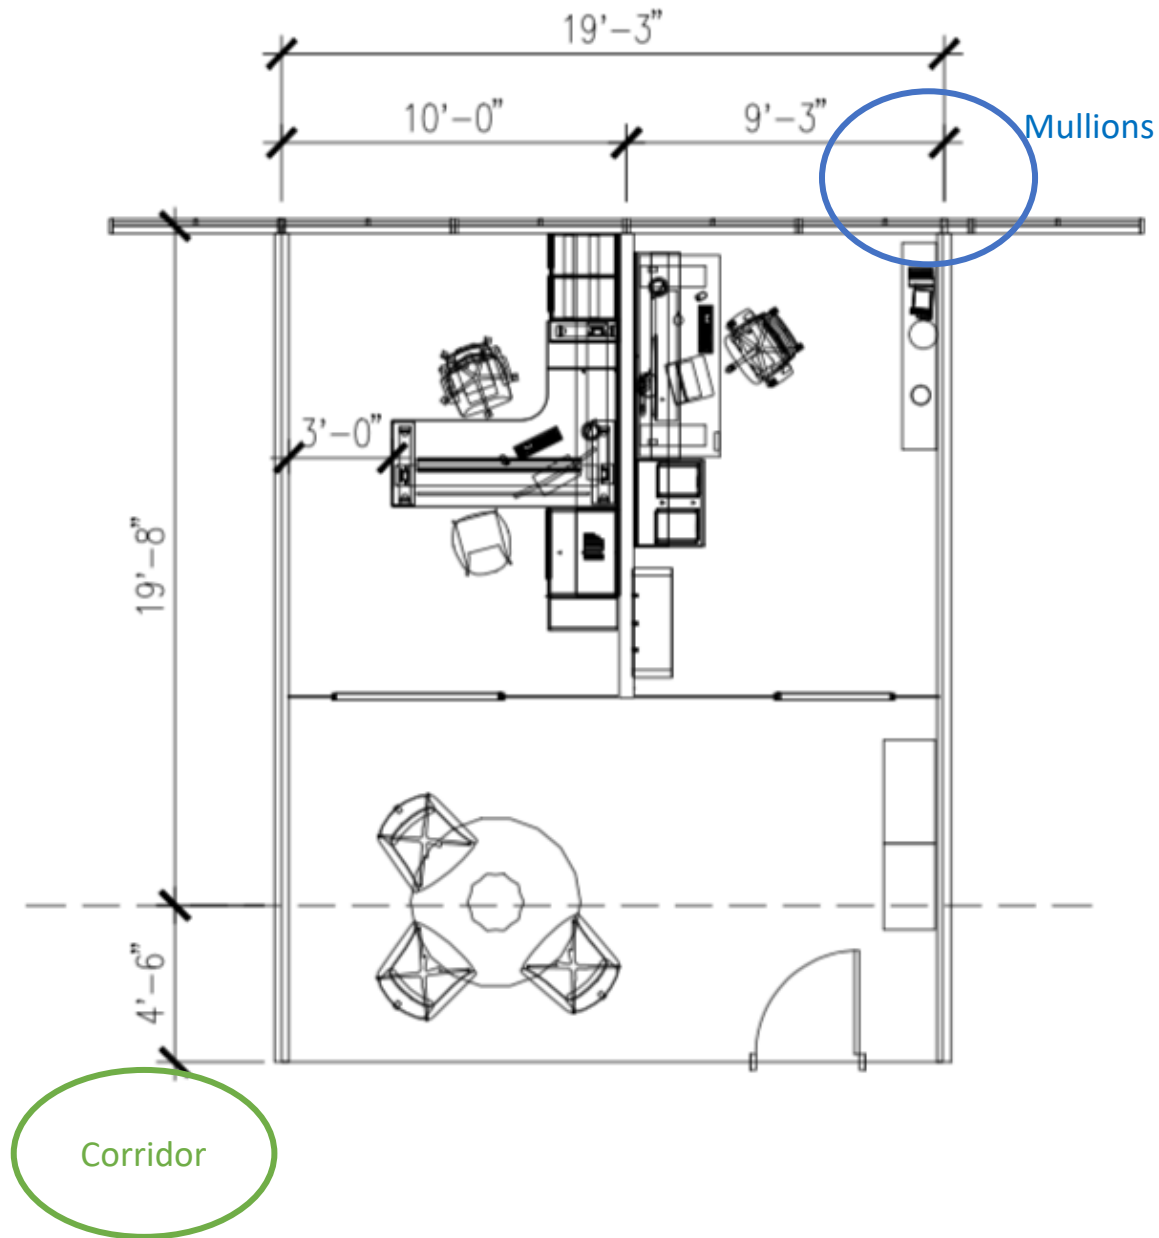

PO 2

465 SF

Private Office
Medium

Size: 43m² (465 SF)

Zone 1 — Habitat: 5.9m (19'8")

Zone 2 — Magazine: 1.3m (4'6")


Zone 3 — Corridor: TBD

Reception: 0

Offices: 2

Workstations: 2 / 22m² (233 SF) per workstation

Occupancy: 6 / 7m² (77 SF) per person

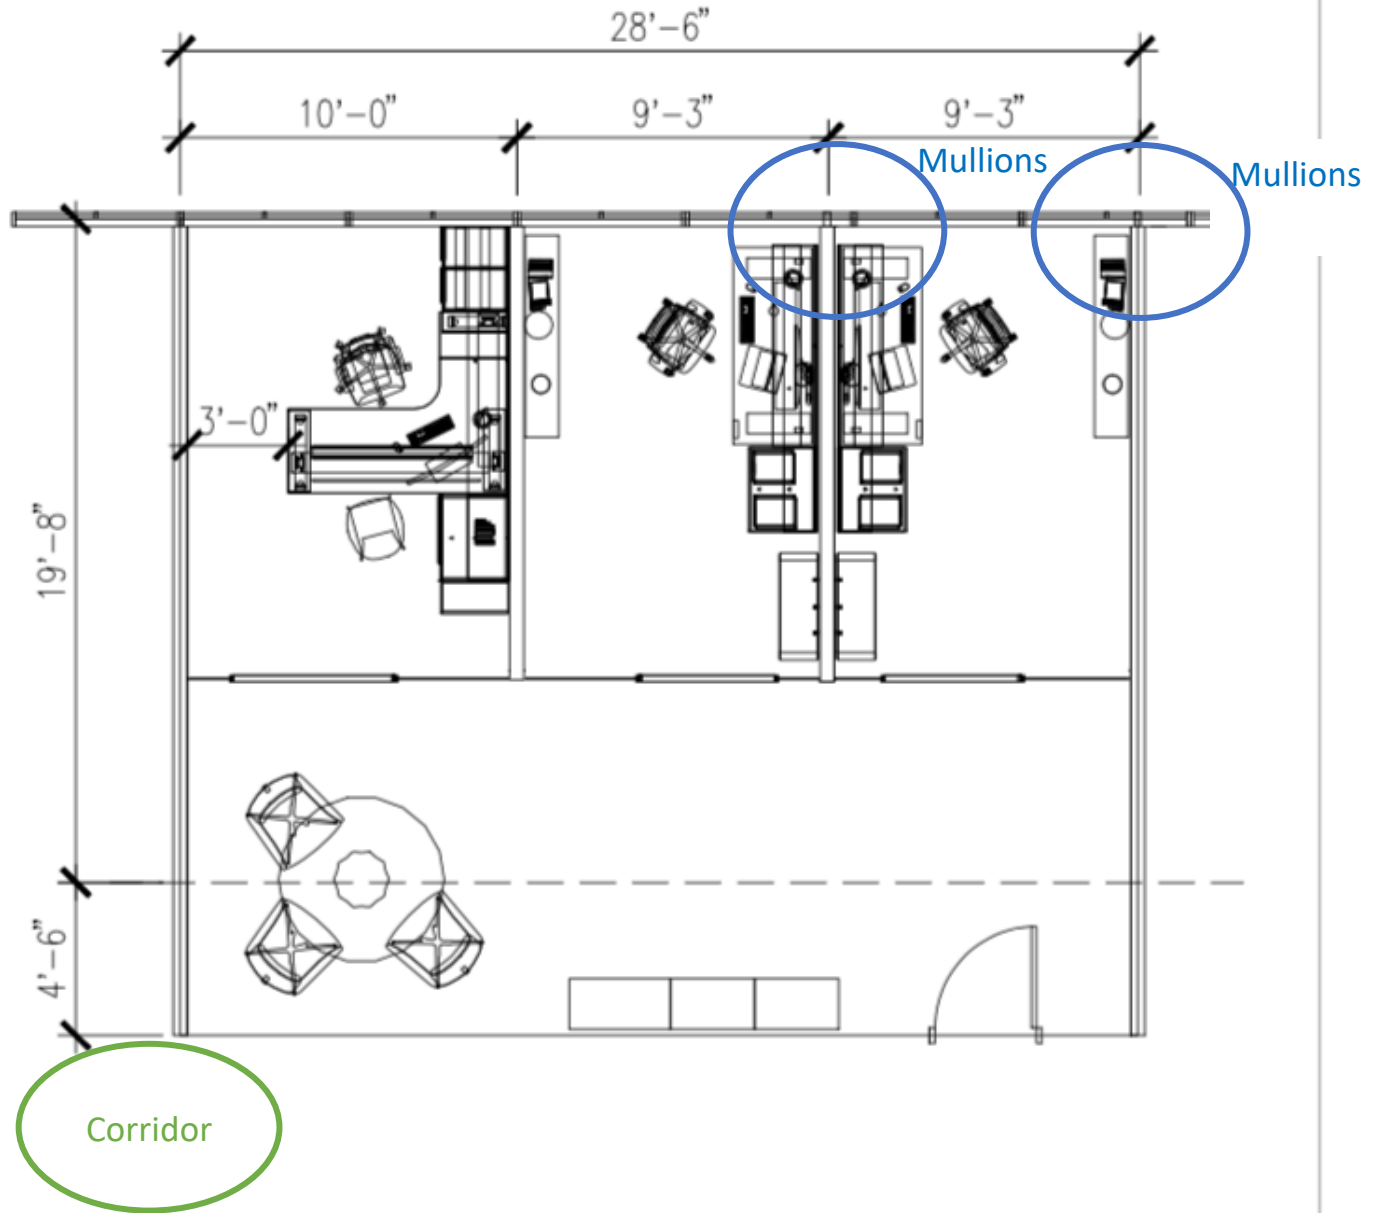

PO 3 **685 SF**

Private Office

Large

Size: 64m² (685 SF)

Zone 1 — Habitat: 5.9m (19'8")

Zone 2 — Magazine: 1.3m (4'6")

Zone 3 — Corridor: TBD


Reception: 0

Offices: 3

Workstations: 3 / 21m² (228 SF) per workstation

Occupancy: 7 / 9m² (97 SF) per person

** With desks placed perpendicular to the façade, be careful, as an extra 0.7metres is required for proper circulation for three desks in series in Zone 1—Habitat. Without accounting for circulation, 6 metres exactly to the façade results in only two desks perpendicular to the façade in Zone 1—Habitat rather than three desks.

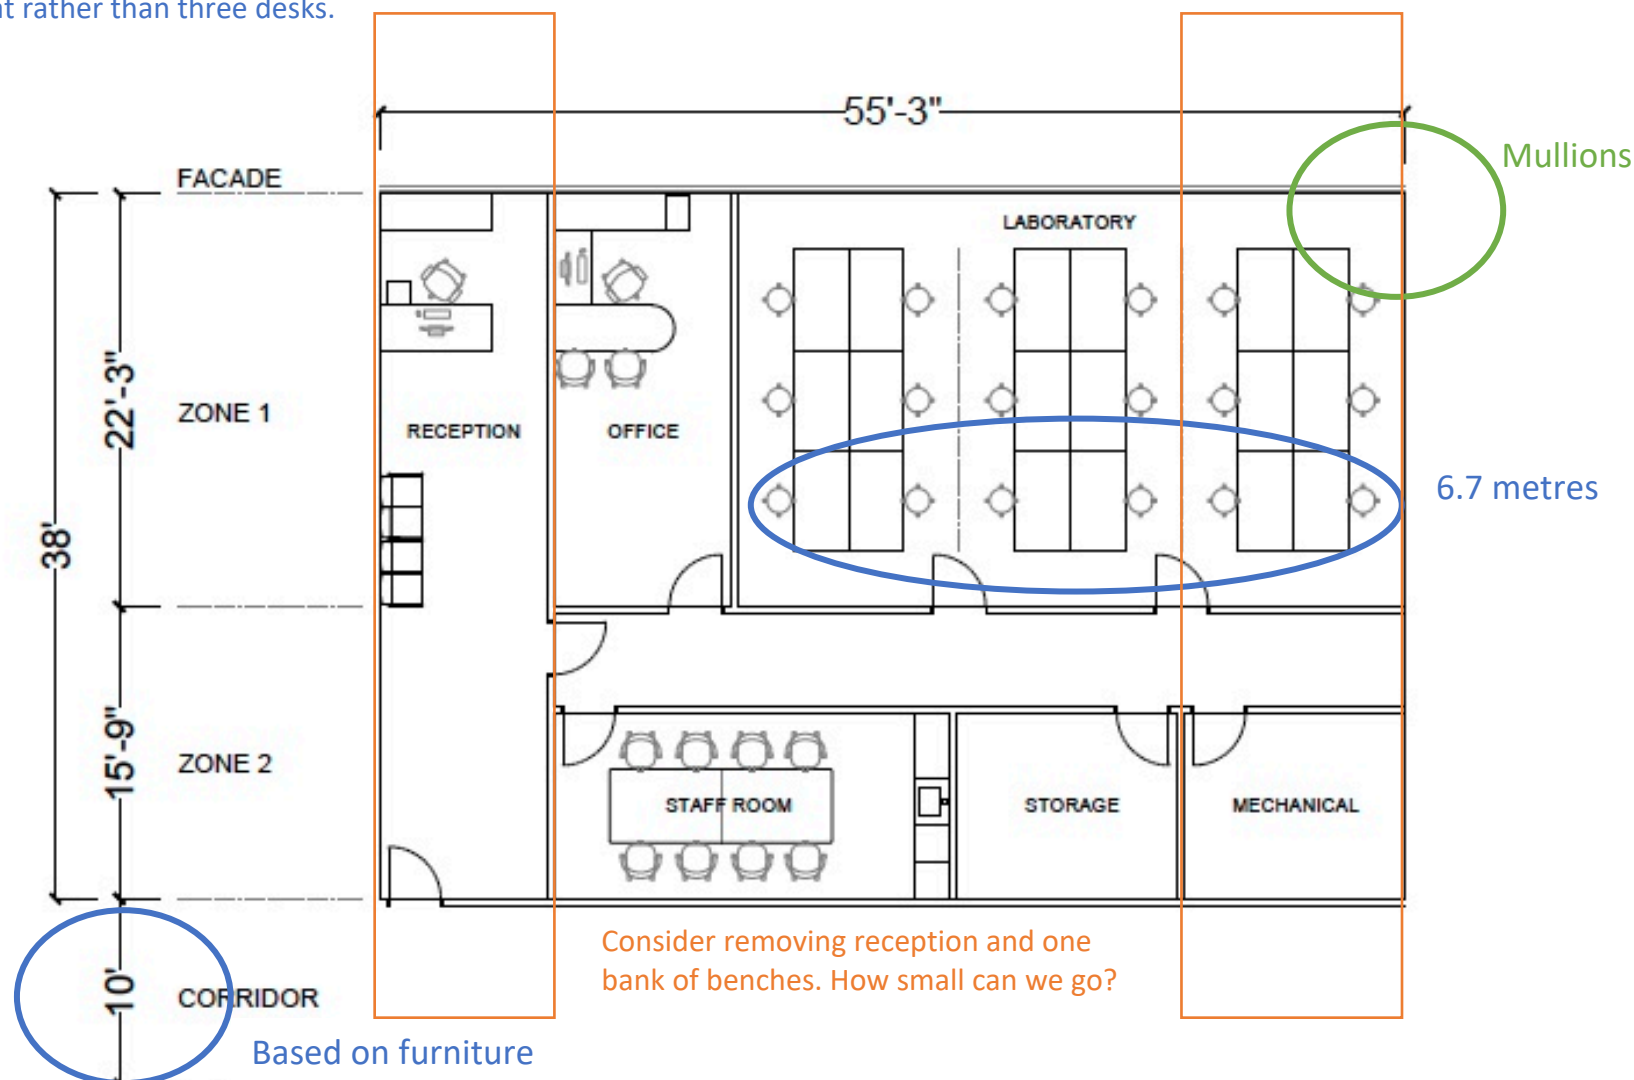Professional Office — Laboratory
Small

Size: ~117 m² (~1,259 SF)

Zone 1 — Habitat: 6.7m (22'3")

Zone 2 — Magazine: 4.8m (15'9")

Zone 3 — Corridor: 3.1m (10')

Reception: 0

Offices: 1

Workstations: 13 / ~9.0m² (~96 SF) per workstation

Occupancy: 24 / ~4.8m² (~52 SF) per person

b | 2099 SF

Professional Office — Laboratory
Small

Size: 195 m² (2,099 SF)

Zone 1 — Habitat: 6.7m (22'3")

Zone 2 — Magazine: 4.8m (15'9")

Zone 3 — Corridor: 3.1m (10')


Reception: 1

Offices: 1

Workstations: 20 / 9.7m² (104 SF) per workstation

Occupancy: 34 / 5.7m² (61 SF) per person

** With desks placed perpendicular to the façade, be careful, as an extra 0.7metres is required for proper circulation for three desks in series in Zone 1—Habitat. Without accounting for circulation, 6 metres exactly to the façade results in only two desks perpendicular to the façade in Zone 1—Habitat rather than three desks.

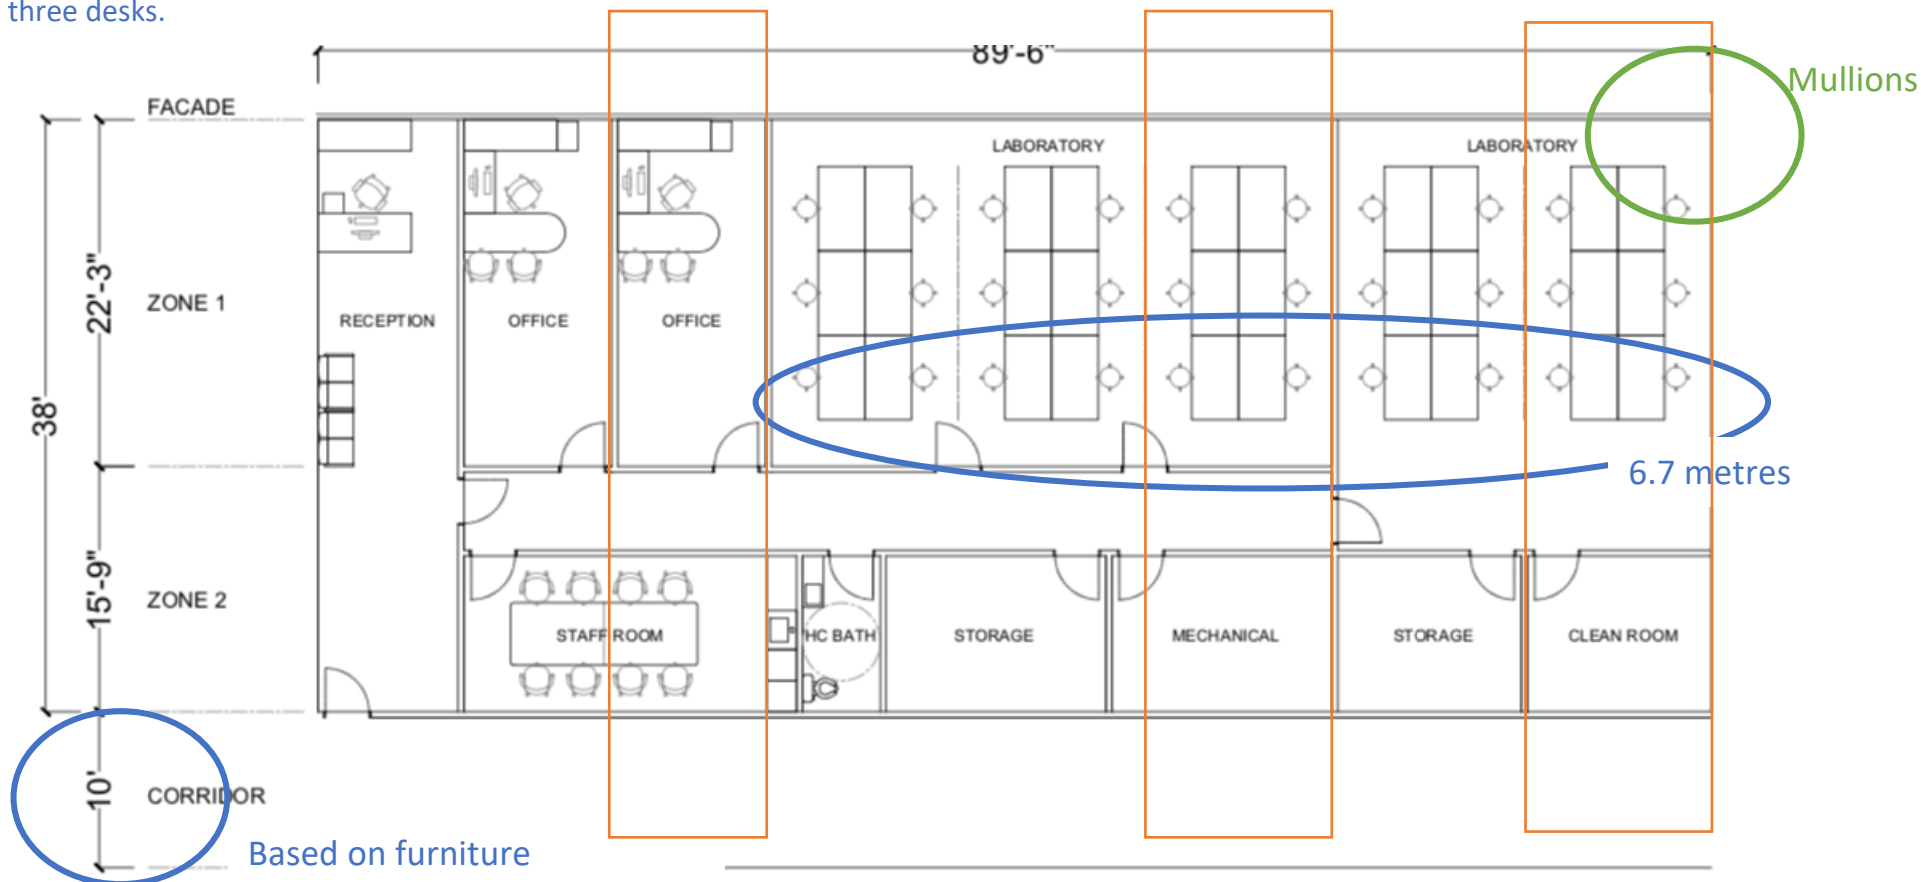

Medium Lab I 3401 SF

Professional Office — Laboratory
Medium

Size: ~242m² (~2,604 SF)

Zone 1 — Habitat: 6.7m (22'3")

Zone 2 — Magazine: 4.8m (15'9")

Zone 3 — Corridor: 3.1m (10')

Reception: 1

Offices: 1

Workstations: 20 / ~12.1m² (~130 SF) per workstation

Occupancy: 29 / ~8.3m² (~89 SF) per person

Professional Office — Laboratory
Medium

Size: 316m² (3,401 SF)

Zone 1 — Habitat: 6.7m (22'3")

Zone 2 — Magazine: 4.8m (15'9")

Zone 3 — Corridor: 3.1m (10')


Reception: 1

Offices: 2

Workstations: 33 / 9.5m² (97 SF) per workstation

Occupancy: 49 / 6.4m² (69 SF) per person

** With desks placed perpendicular to the façade, be careful, as an extra 0.7metres is required for proper circulation for three desks in series in Zone 1—Habitat. Without accounting for circulation, 6 metres exactly to the façade results in only two desks perpendicular to the façade in Zone 1—Habitat rather than three desks.

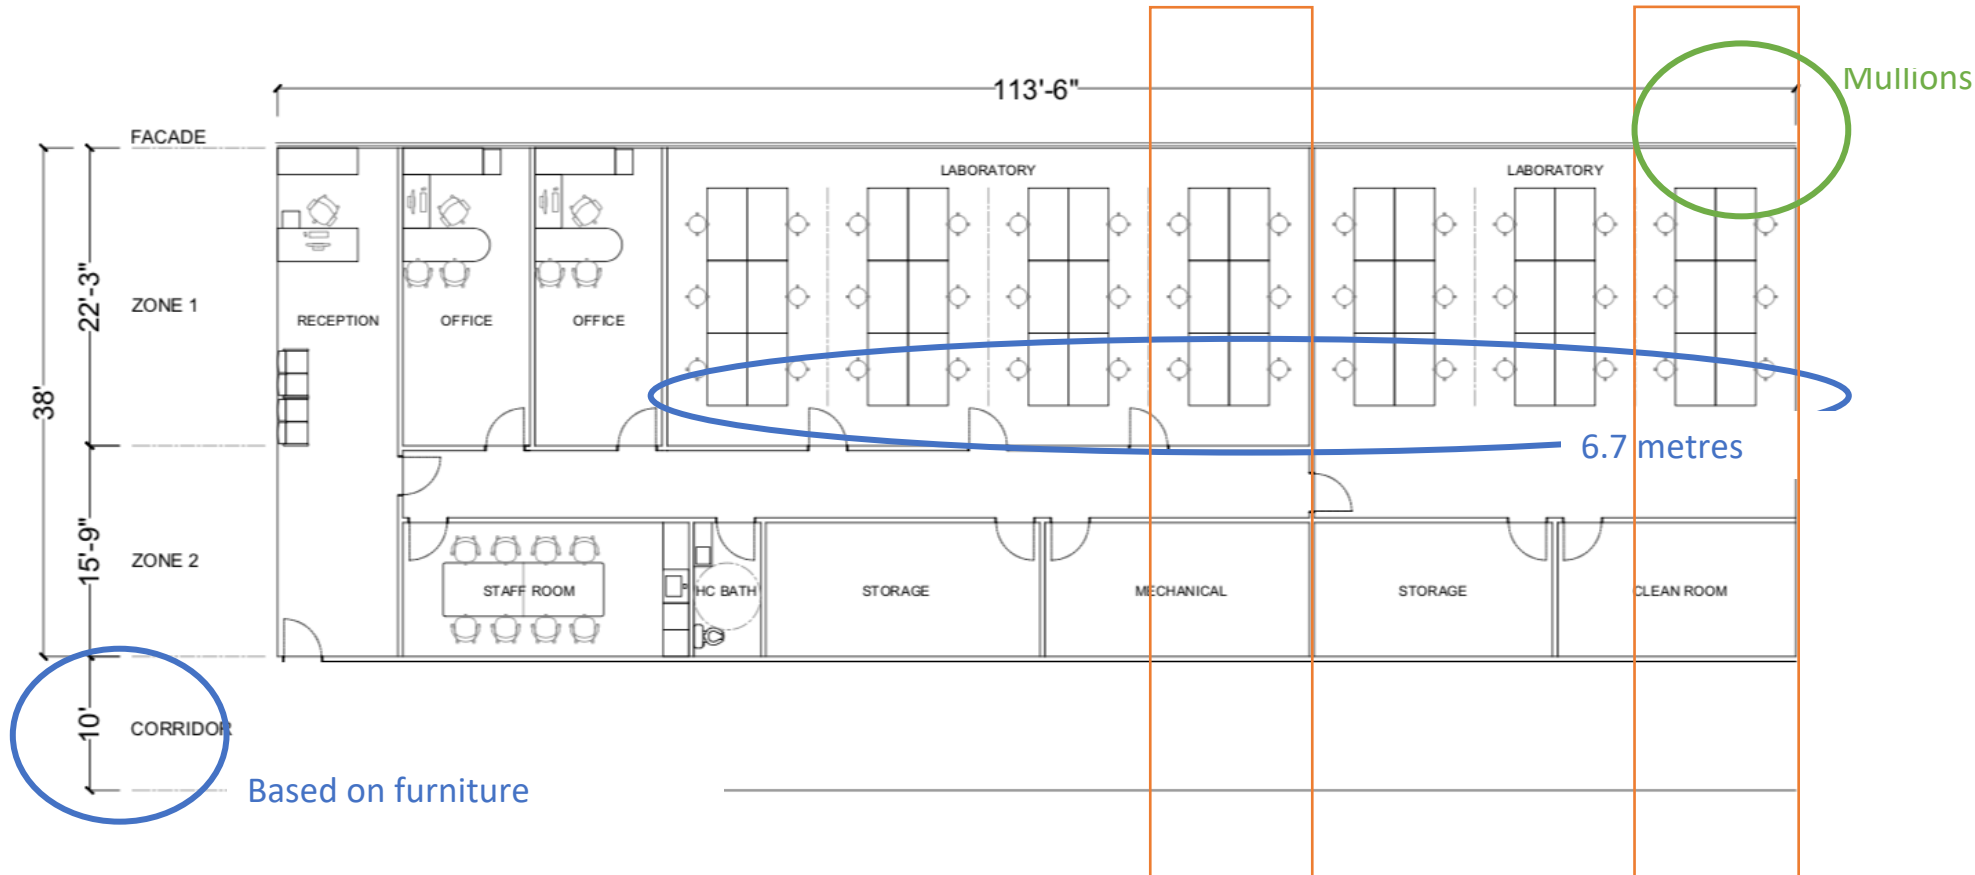

Large Lab | 4313 SF

Professional Office — Laboratory

Large

Size: ~287m² (3,089 SF)

Zone 1 — Habitat: 6.7m (22'3")

Zone 2 — Magazine: 4.8m (15'9")

Zone 3 — Corridor: 3.1m (10')

Reception: 1

Offices: 2

Workstations: 33 / ~8.1m² (~93 SF) per workstation

Occupancy: 49 / ~5.8m² (~63 SF) per person

Professional Office — Laboratory

Large

Size: 401m² (4,313 SF)

Zone 1 — Habitat: 6.7m (22'3")

Zone 2 — Magazine: 4.8m (15'9")


Zone 3 — Corridor: 3.1m (10')

Reception: 1

Offices: 2

Workstations: 45 / 8.9m² (95 SF) per workstation

Occupancy: 61 / 6.5m² (70 SF) per person

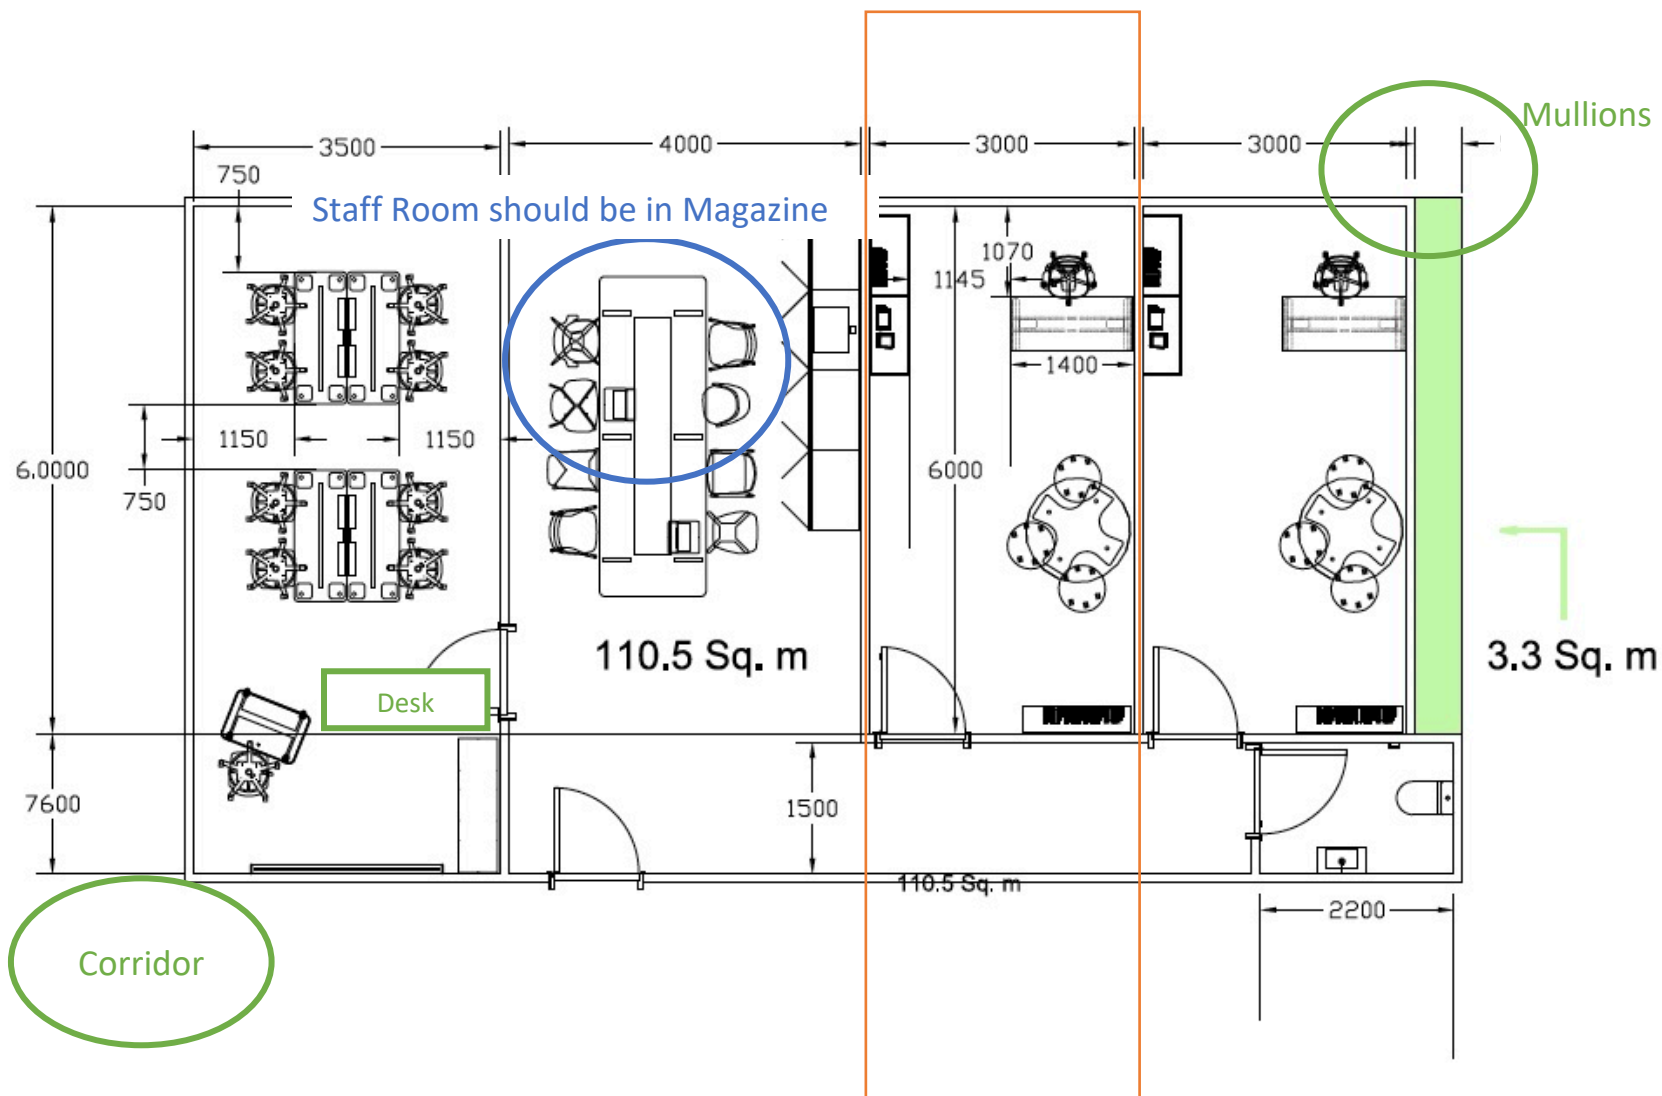

Professional Office — Academic Small

Size: ~87.7m² (944 SF)

Zone 1 — Habitat: 4.7m (15'5")

Zone 2 — Magazine: 3.0m (9'10")

Zone 3 — Corridor: TBD

Reception: 0

Offices: 1

Workstations: 2 / ~43.8m² (472 SF) per person

Occupancy: 21 / 4.1m² (44 SF) per person

Professional Office — Academic Small

Size: 110.5m² (1,189 SF)

Zone 1 — Habitat: 4.7m (15'5")

Zone 2 — Magazine: 3.0m (9'10")


Zone 3 — Corridor: TBD

Reception: 0

Offices: 2

Workstations: 3 / 36.8m² (396 SF) per person

Occupancy: 25 / 4.4m² (47 SF) per person

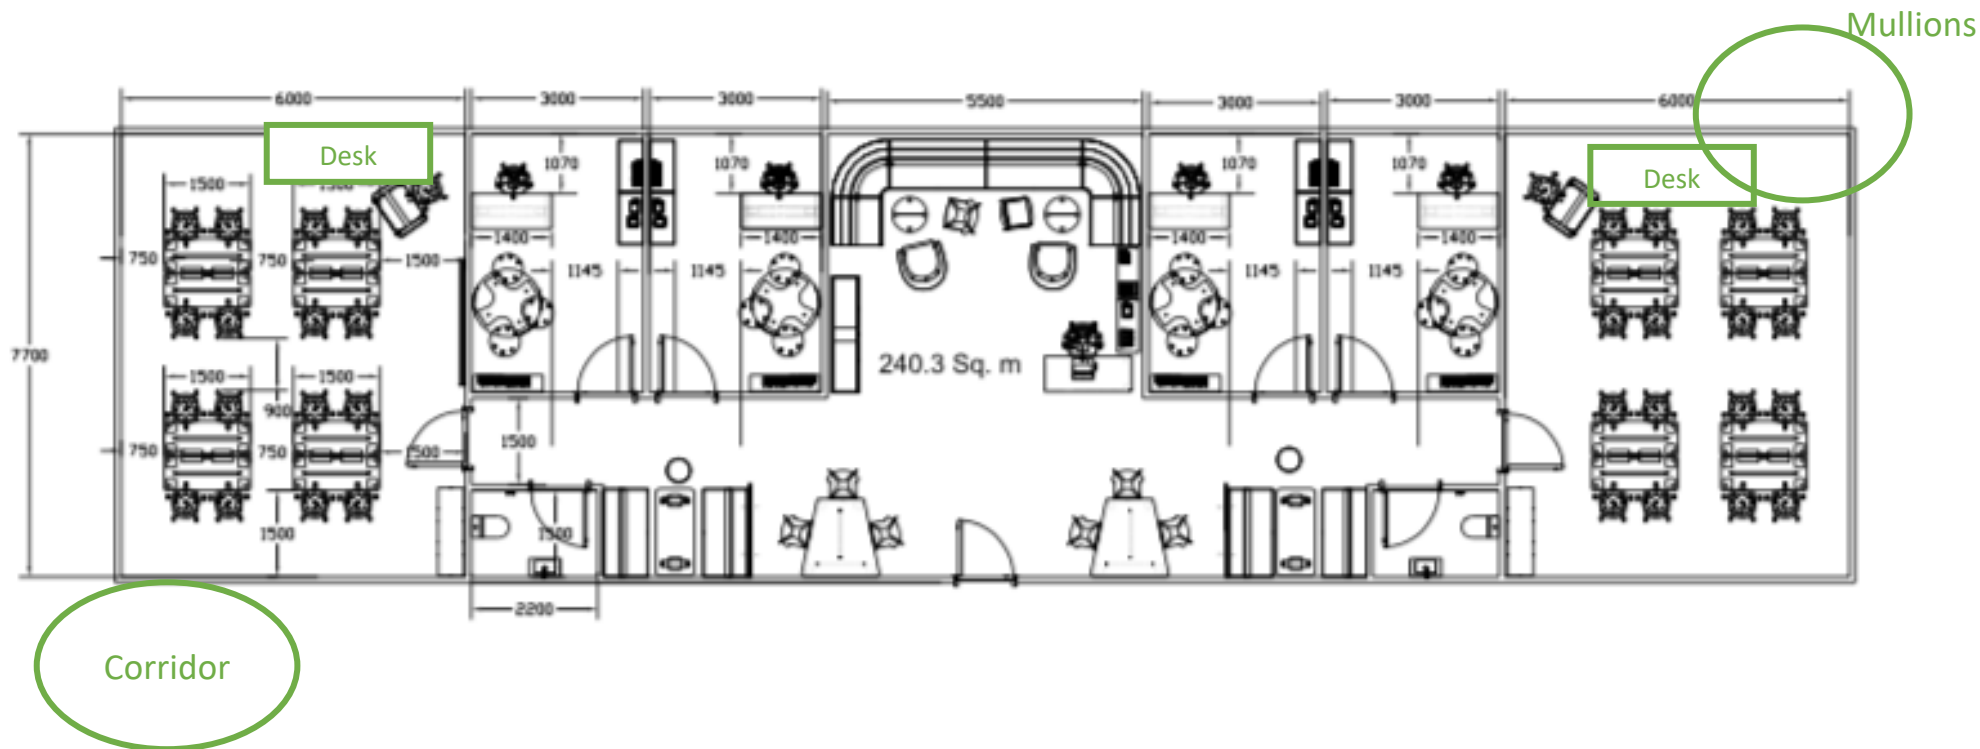

Professional Office — Academic
Medium

Size: 240.3m² (2,586 SF)

Zone 1 — Habitat: 4.7m (15'5")

Zone 2 — Magazine: 3.0m (9'10")


Zone 3 — Corridor: TBD

Reception: 1

Offices: 4

Workstations: 7 / 34.3m² (369 SF) per workstation

Occupancy: 63 / 3.8m² (41 SF) per person

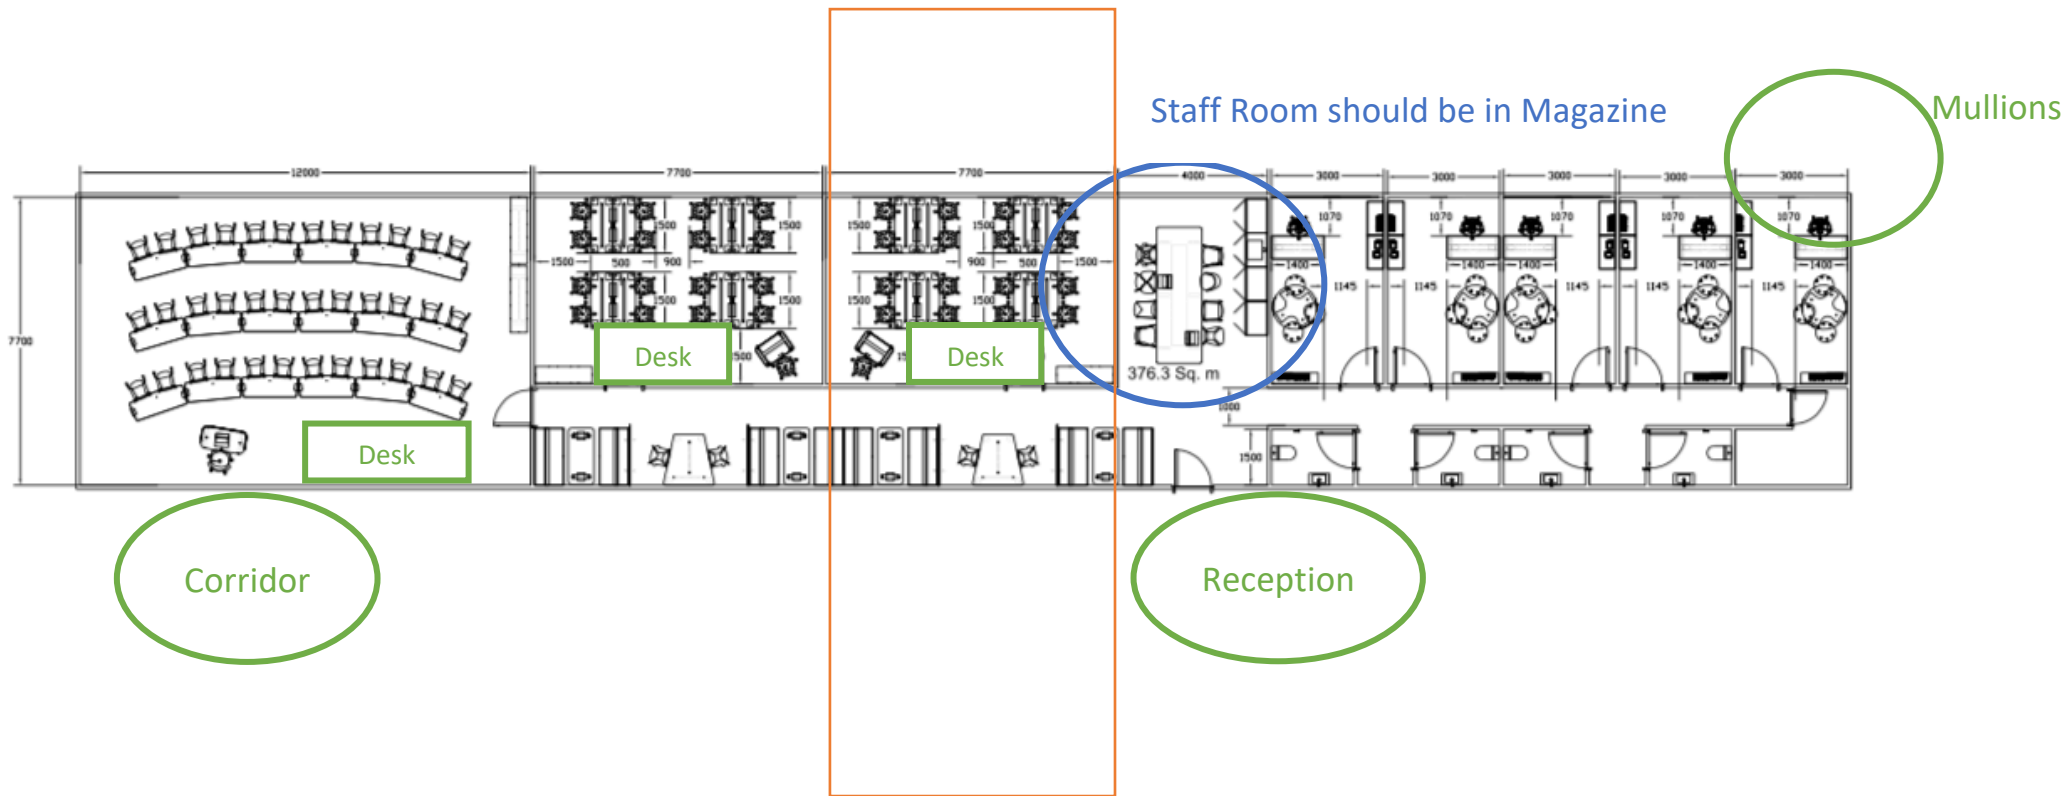

Professional Office — Academic
Large

Size: $\sim 327.3\text{m}^2$ ($\sim 3,523$ SF)

Zone 1 — Habitat: 4.7m (15'5")

Zone 2 — Magazine: 3.0m (9'10")

Zone 3 — Corridor: TBD

Reception: 0

Offices: 5

Workstations: 7 / $\sim 46.7\text{m}^2$ (503 SF) per workstation

Occupancy: 82 / $\sim 3.9\text{m}^2$ (43 SF) per person

Consider removing one seminar?

Professional Office — Academic
Large

Size: 376.3m^2 (4,050 SF)

Zone 1 — Habitat: 4.7m (15'5")

Zone 2 — Magazine: 3.0m (9'10")

Zone 3 — Corridor: TBD

Reception: 0

Offices: 5



Workstations: 8 / 47.0m^2 (506 SF) per workstation

Occupancy: 103 / 3.6m^2 (39 SF) per person

Medical M 3

small - 2 dental chairs

2'401.5 sq ft

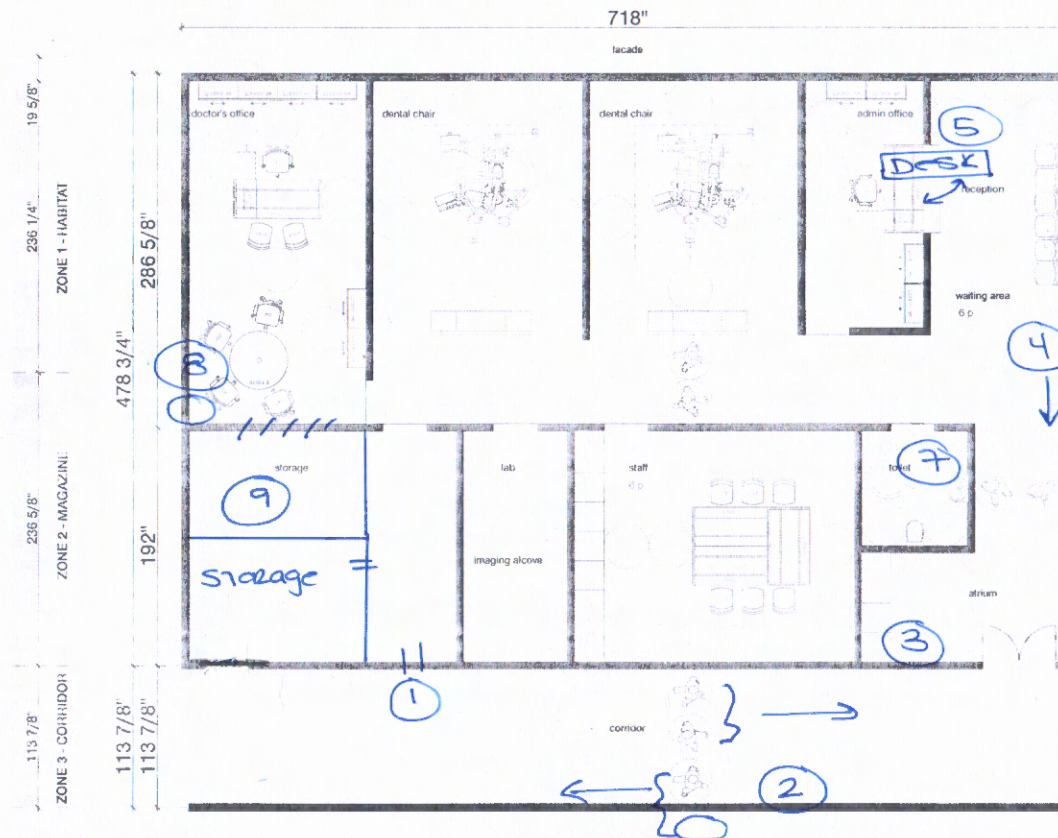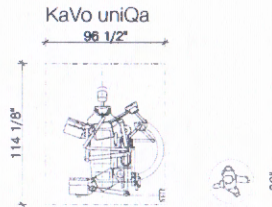



- mechanical Room
- Workbench with 2-3 seats and SINKS
- Autoclave (sterilization)
- Imaging Room
- File Room
- Storage Room
- inventory

- ① ADD SECOND DOOR FOR emergencies
- ② ADD "bubble" FOR 4 people
• what is the MAX?
• 2 each way
- ③ LINE OF SIGHT - Safety
Reception needs to see the clock
- ④ ADD "Bubble" TO OFFICE table
- ⑤ Extend office into Zone #2

Medical
M 1

medium - 4 dental chairs


3'567.7 sq ft

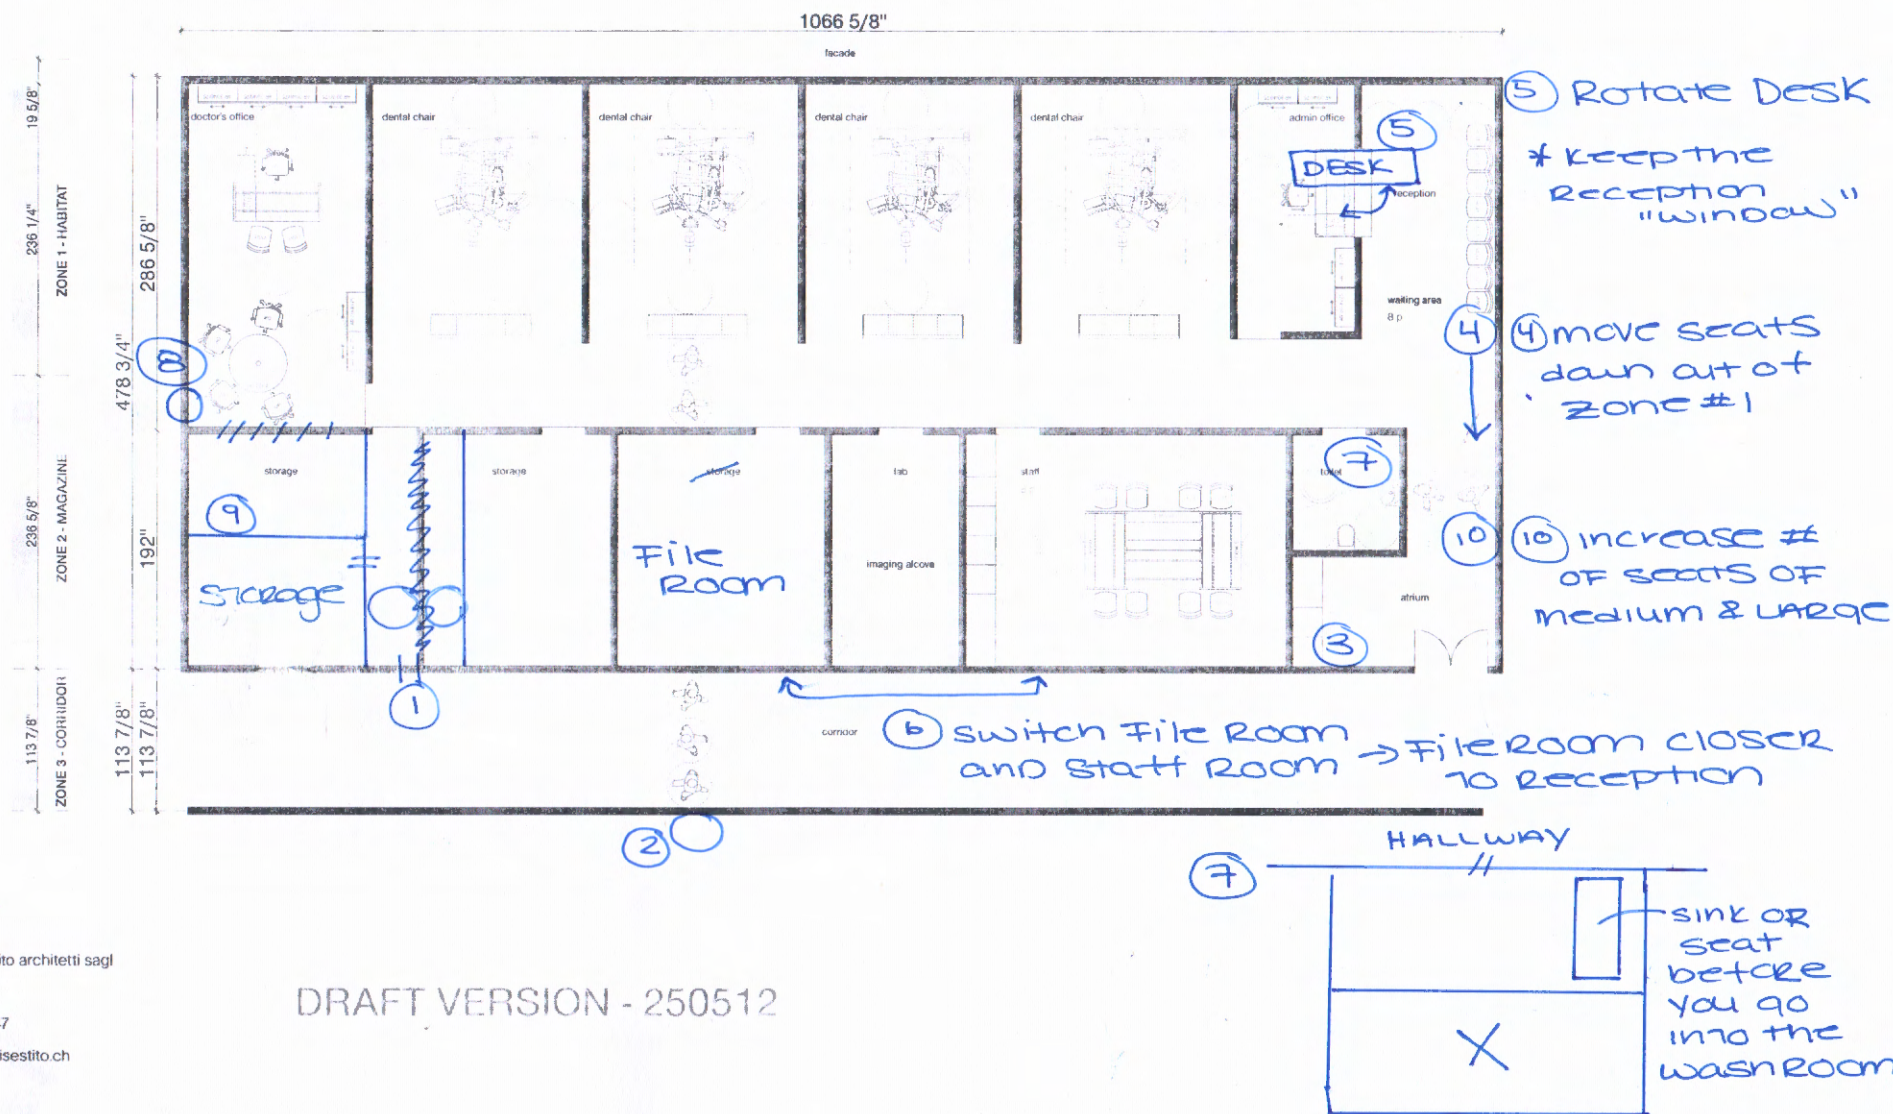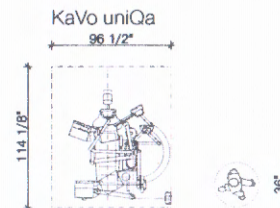

Medical M 2


large - 6 dental chairs

5'231.4 sq ft

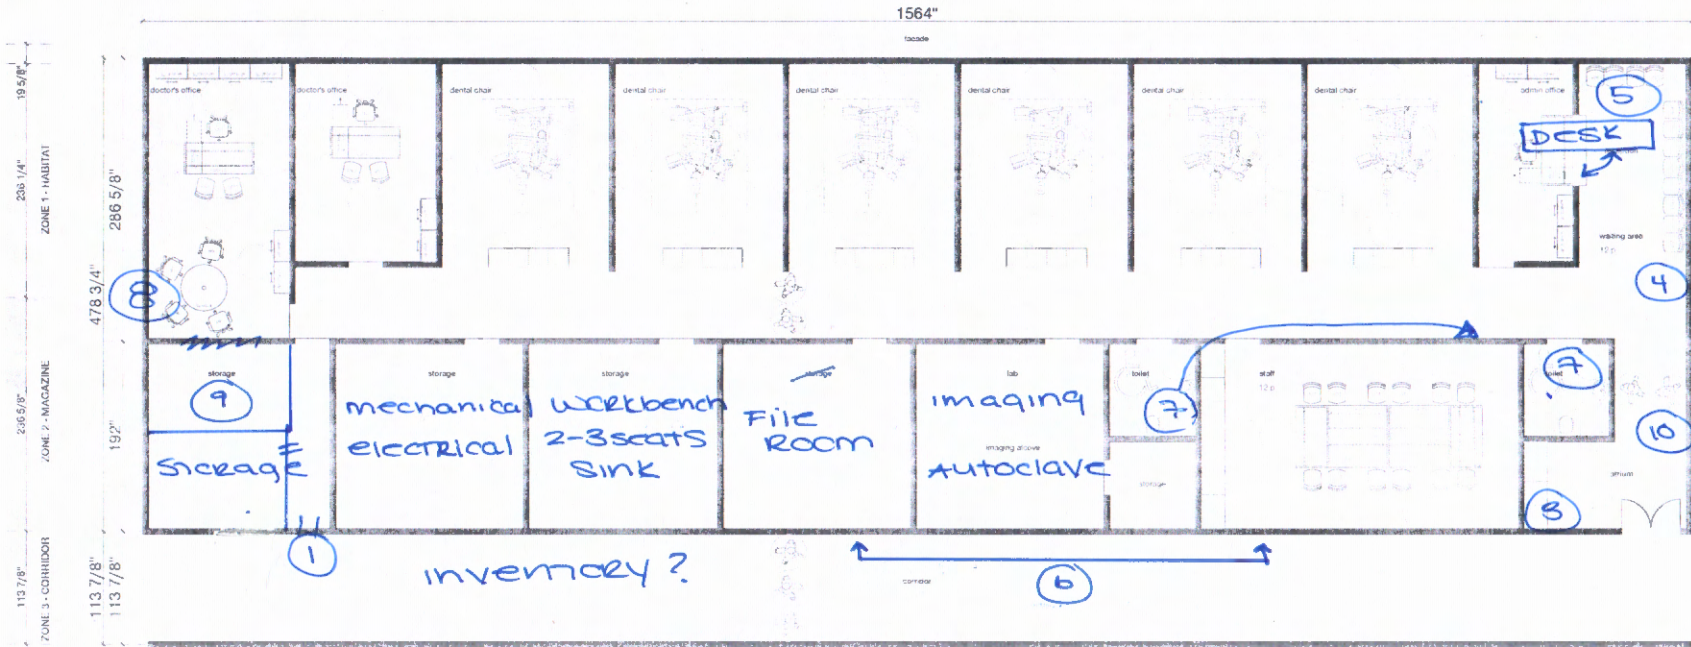

②

⑦ move washrooms together
HALLWAY

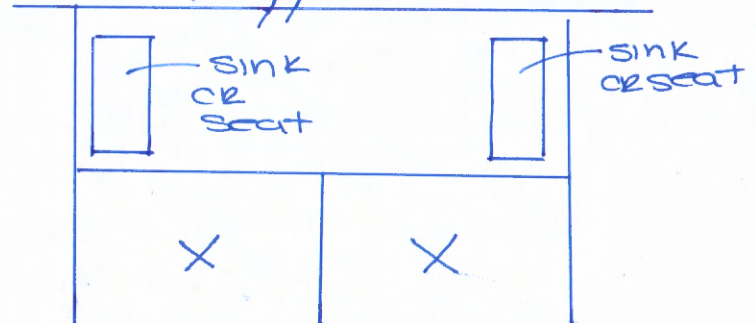

DRAFT VERSION - 250512

NTD: The way to reduce the depth of Zone 2 — Magazine would be to choose a smaller table, a narrower table, for the Staff Room, but still a real table from Steelcase. To change the dimensions, we need to use furniture, real furniture, that is easily accessible, widely used and affordable.

NTD: Need to ensure that when the space is given back by a Tenant, we can provide the next tenant with a space that can get all certificates. The "gold standard" is always achievable.

NTD: We can better define the minimum floor-to-ceiling height needed to support the user's well-being once the Key Plans are in place.

NTD: If a tenant truly felt they were being forced to take too much space, we could use the Key Plans to check and they could shade out the area they did not want, and we could discount the rent accordingly — the rates applied to the Magazine should not be the same as those applied to the Habitat.

Mechanical Room

Workbench with two/three seats and sink

Autoclave

Imaging Room

Inventory

Storage Room

File Room